
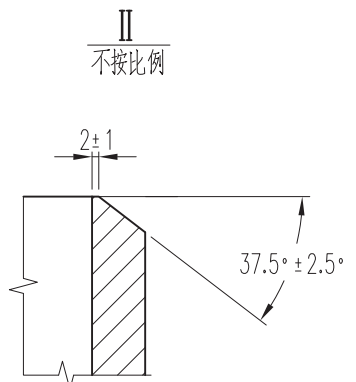
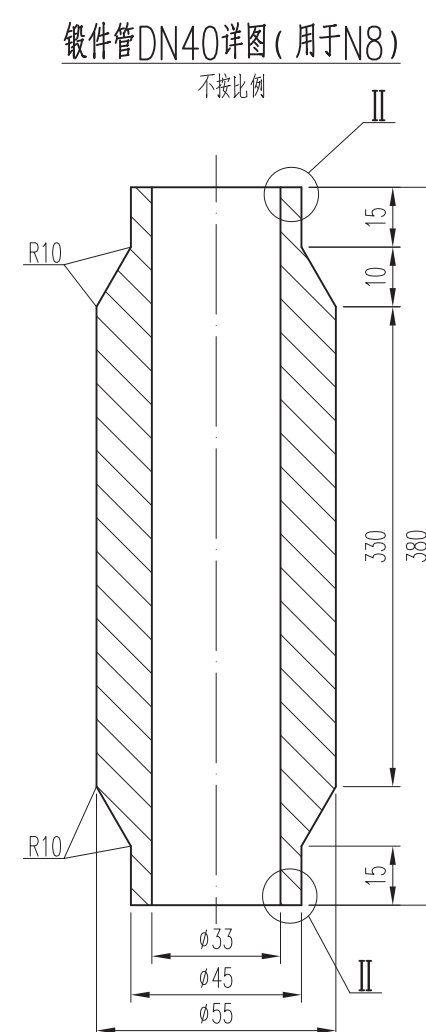
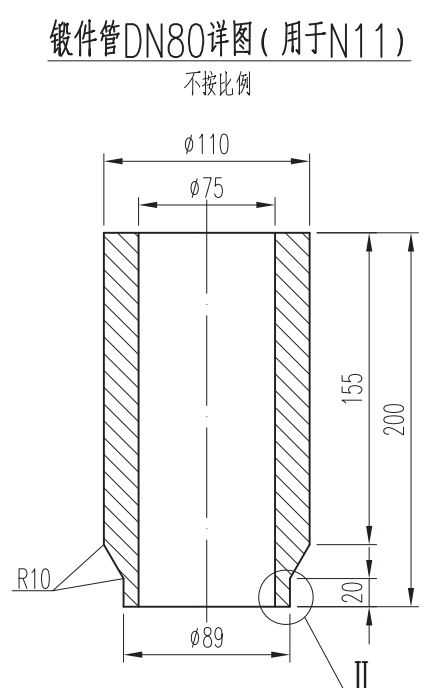


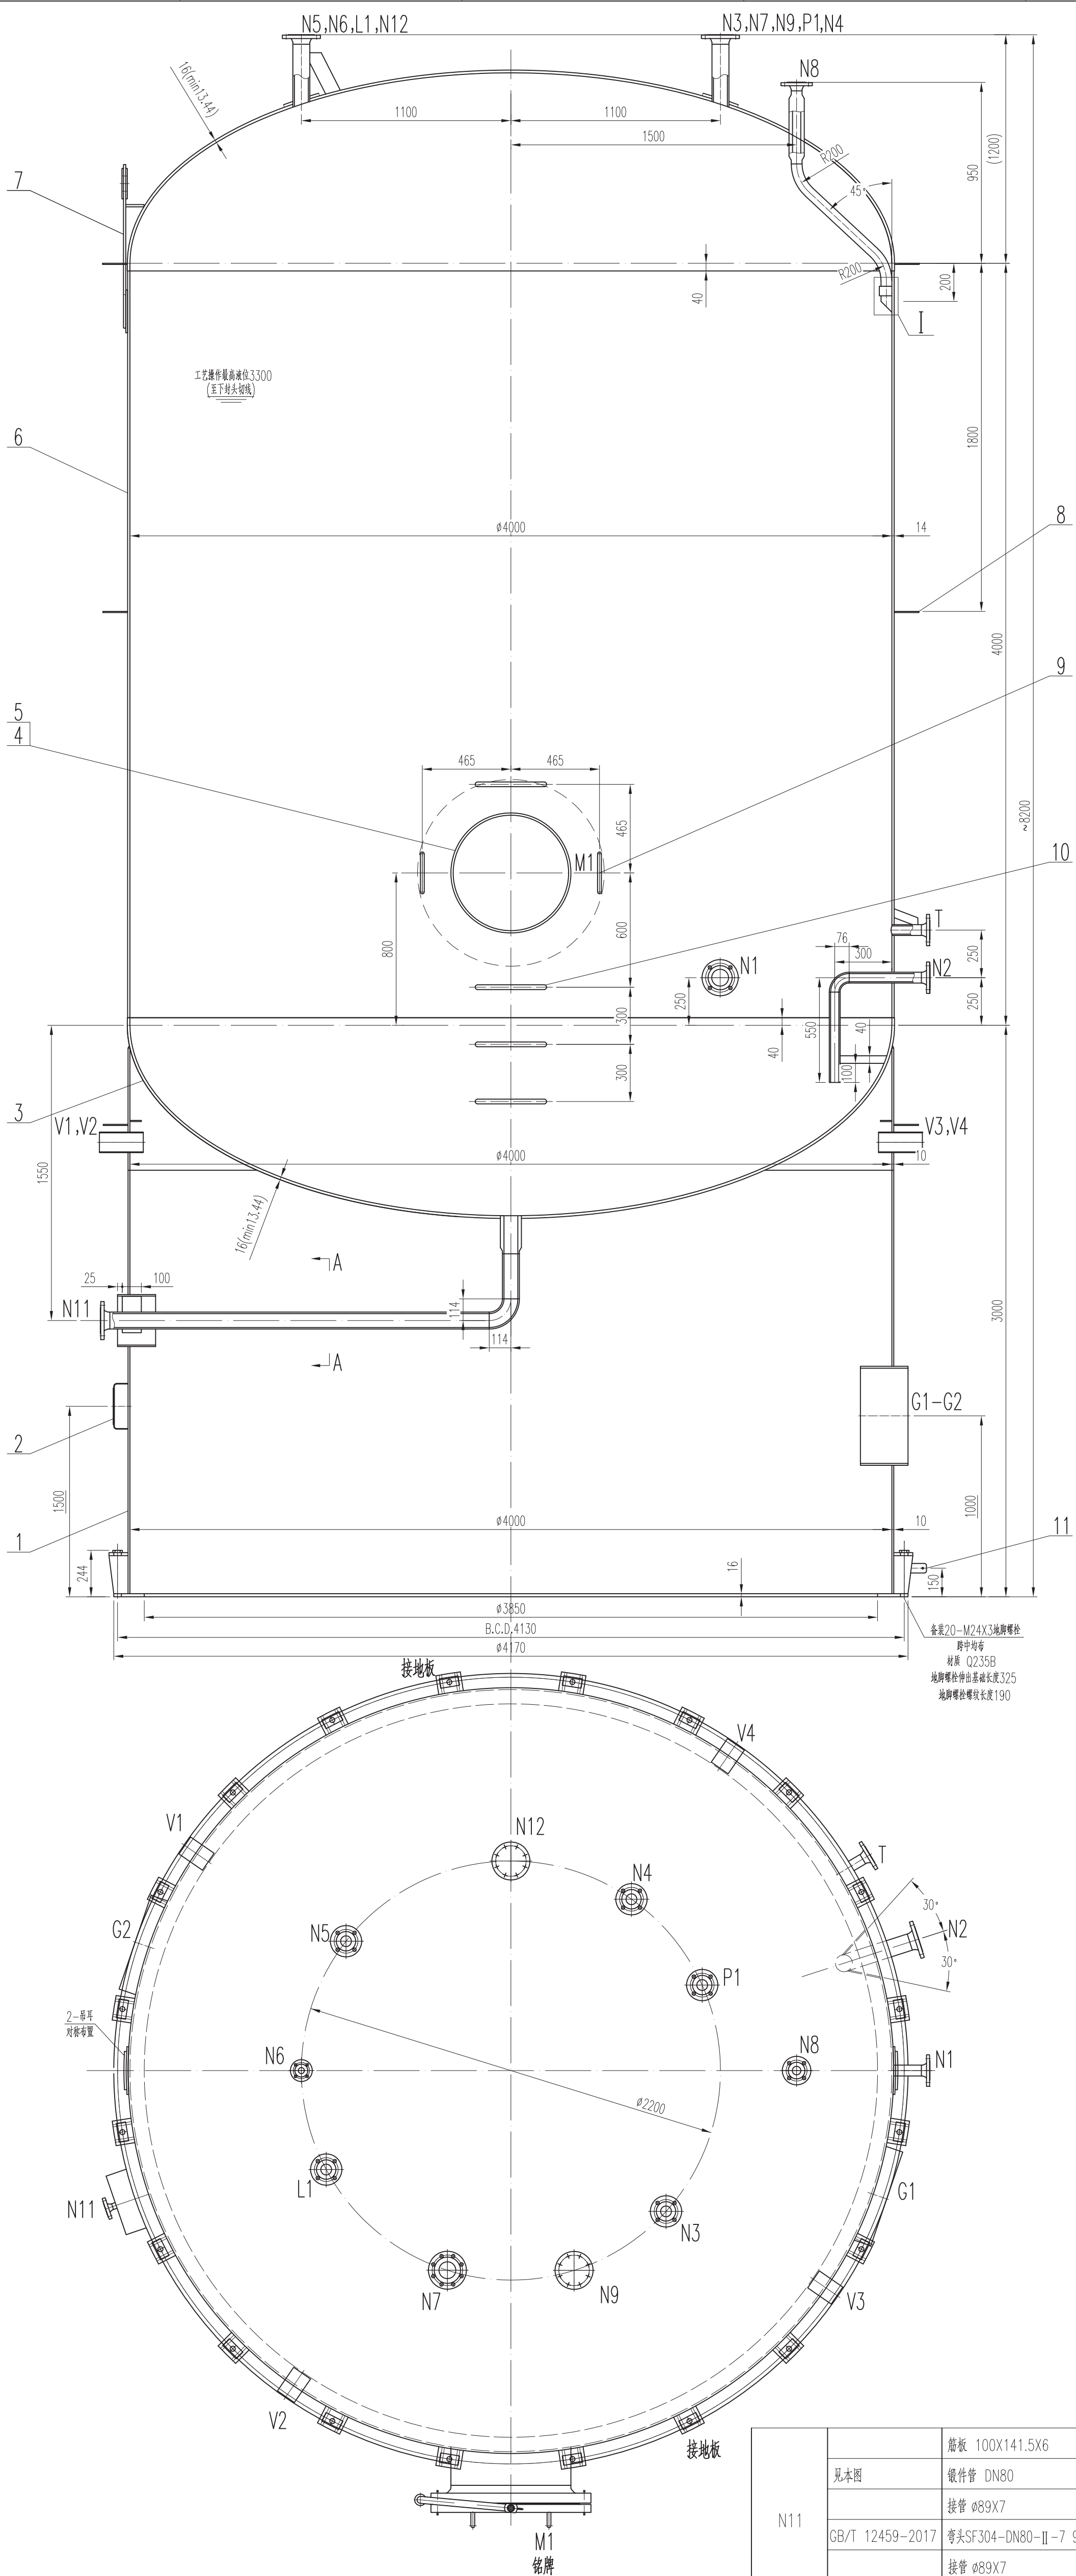

REGULATION 规范 CODE & STD.	GB/T 150.1~GB/T 150.4-2011,参照NB/T 47041-2014《板式容器》										REQUIREMENTS FOR FABRICATION, TESTING AND INSPECTION				设计数据 DESIGN DATA				零件 COLUMN								
制造、检验要求														压力容器类别 CATEGORY				--		类 CATEGORY							
承压元件用钢板应符合《承压/临海承压钢板用钢板》 STEEL PLATES USED FOR PRESSURE PARTS IN DWG. SPEC./GRADE/PLATE														压力容器级别 CLASS				--		级 CLASS							
焊接接头 WELDING JOINT SPECIFICATION														NB/T 47015-2011													
焊接接头结构标准 WELDING JOINT SPECIFICATION														除注明者外, 按 GB/T 20583-2020				设计使用年限 DESIGN LIFE				15年					
对接接头长度 GUE LENGTH OF JOINT WELD														除注明者外, 两相组件中较薄件的厚度				工作压力 OPER. PRESSURE				MPa(G)		常压			
法兰的焊接结构 WELDING BETWEEN FLANGE TO PIPING														按相应法兰标准				设计压力 DESIGN PRESSURE				MPa(G)		0.6			
焊接材料选择标准 WELDING MAT'L SPECIFICATION														NB/T 47015-2011, NB/T 47018.4-2017 NB/T 47018.1~47018.3, 47018.5-2020				工作温度 OPER. TEMPERATURE				℃		常温			
无损检测标准 NONDESTRUCTIVE TESTING SPECIFICATION														NB/T 47013.1~47013.5-2015				设计温度 DESIGN TEMPERATURE				℃		60			
无 损 探 伤 NOT	焊接接头类型 JOINT CATEGORY		检测方法 METHOD		检测率 RATIO		技术等级 REAL. GRADE		质量等级 QUALITY GRADE		安全裕度压力 SET-UP PRESSURE OF SAFETY VALVE		MPa(G)		0.6												
	A、B类焊接接头		RT		20%, ≥250mm		AB		III		最高允许工作压力 MAXIMUM ALLOWABLE WORKING PRESSURE		MPa(G)		--												
	D、E类焊接接头		PT		100%		--		I		名称 NAME		乙二胺														
	DN<250罐壁与罐底 罐壁与罐底之间的角焊缝		PT		100%		--		I		密度 DENSITY		kg/m ³		900												
	充装前及充装后必须经无损检测合格		PT		100%		--		I		介 MEDIUM		毒性危害程度 TOXICITY		中轻度危害												
焊后热处理标准 P.W.H.T. SPECIFICATION														--				焊接接头系数 EXPLOSIVE				原爆					
焊后消除应力热处理要求 P.W.H.T. REQUIREMENT														--				耐腐蚀性 CORROSION ALLOWANCE				mm		0			
耐压试验 PRESSURE TEST														水压试验压力 HYDROSTATIC TEST PRESSURE				MPa(G)		0.75(±)/0.81(±)							
														气压试验压力 PNEUMATIC TEST PRESSURE				MPa(G)		--							
泄漏试验要求 LEAK TEST REQUIREMENT														MPa(G)				--				容积 CAPACITY		m ³		67.02(注1)	
表面处理要求 SURFACE TREATMENT REQUIREMENT														内表面 INT. SURF.		0321083-000-0000-PM-012-002		充装系数 FILLING EFFICIENCY		--							
外表面涂装要求 EXTERNAL SURFACE PAINTING REQUIREMENT														0321083-000-0000-PM-012-002		基本风压 REFERENCE WIND PRESSURE		N/m ²		500							
运输包装标准 PACKING FOR TRANSPORT														NB/T 10558-2021				抗震性能 SEISMIC RESISTANCE				A					
现场组焊标准 ASSEMBLING AND WELDING SPEC.														--				抗震设防烈度/设计地震分组 SEISMIC FORTIFICATION INTENSITY/GROUP				7度/二组					
安装质量检验标准 QUALITY INSPECTION OF ERECTION														GB 50461-2008				设计基本地震加速度 DESIGN BASIC ACCELERATION OF GROUND MOTION				0.16g					
管口方位 ORIENTATION														按管口方位图(特定)				场地土类别 FIELD SOIL CATEGORY				IV					
支筒防火要求 FIREPROOF REQUIREMENT														罐体对外(见其它技术要求7)				年平均最高气温的最低值 MINIMUM MONTHLY MEAN TEMPERATURE				--4.9					
安全附件及仪表 SAFETY ACCESSORIES														本设备已考虑安全阀				绝热厚度 INSULATION THICK.				mm		130			
注: 设计使用年限是指在正常工况操作及正常维护条件下, 根据设计人对于金属壁的平均腐蚀速率不大于腐蚀裕量所确定的容器使用寿命。 NOTE: DESIGN LIFE DETERMINED UNDER NORMAL AND STABLE OPERATION AND NORMAL MAINTENANCE CONDITIONS FOR THE DESIGNATED SERVICE, WHICH IS NOT LONGER THAN THE CORROSION ALLOWANCE.																											
MATERIALS FOR MAIN PRESSURE PARTS																											
类别 DESCRIPTION	材料牌号 DESIGNATION	材料标准号 MATERIAL STANDARD	供货状态 CONDITION	附加要求 ADDITIONAL REQUIREMENT				空设备质量 EMPTY MASS				kg				14110											
板材	S30408	GB/T24511-2017	固溶					内部可拆件质量 MOVABLE PART MASS				kg				--											
管材	S30408	GB/T14976-2012	固溶					试块时的质量 WATER MASS WHEN TEST				kg				67020											
锻件	S30408	NB/T 47010-2017	固溶	II级																							

符 号	公称压力 PN	公称尺寸 DN	法 兰 标 准	法兰类型 代 号	密封面 型 式	用 途	接管外伸长度 S.F. TO C.L. (外径×壁厚)	接管规格
M1	--	600	--	--	--	人孔	--	φ630X12
N1	16	80(B)	HG/T 20592-2009	WN	RF	物料入口	2250	φ89X7
N2	16	50(B)	HG/T 20592-2009	WN	RF	物料出口	2200	φ57X6
N3	16	50(B)	HG/T 20592-2009	WN	RF	气相平衡口	见图	φ57X6
N4	16	50(B)	HG/T 20592-2009	WN	RF	排气口	见图	φ57X6
N5	16	50(B)	HG/T 20592-2009	WN	RF	安全阀口	见图	φ57X6
N6	16	25(B)	HG/T 20592-2009	WN	RF	氮气入口	见图	φ32X5
N7	16	80(B)	HG/T 20592-2009	WN	RF	检查口	见图	φ89X7
N8	16	40(B)	HG/T 20592-2009	WN	RF	回流口	见图	φ45X6*
N9	16	80(B)	HG/T 20592-2009	WN	RF	备用口(配法兰盖)	见图	φ89X7
N11	16	80(B)	HG/T 20592-2009	WN	RF	排净口	2250	φ89X7
N12	16	80(B)	HG/T 20592-2009	WN	RF	备用口(配法兰盖)	见图	φ89X7
P1	16	50(B)	HG/T 20592-2009	WN	RF	远传压力计口	见图	φ57X6
L1	16	100(B)	HG/T 20592-2009	WN	RF	雷达液位计口	见图	φ108X10
T	16	40(B)	HG/T 20592-2009	WN	RF	远传温度计口	2250	φ45X6
G1,G2	--	600	--	--	--	螺栓检查孔	--	--
V1-V4	--	100	--	--	--	排气管	--	--

*该尺寸为接管与法兰连接处颈部尺寸。

自控	沈少宇	2023.2.15
管道		2023.2.15
工艺		2023.2.15
专业 DISP.	会签人 COUNTERSIGN	日期 DATE
专业负责人		
项目负责人		

N5	HG/T 20592-2009	法兰 WN 50(B)-16 RF S=6	1	S30408II		2.5	
		接管 $\phi 57 \times 6$	1	S30408		2.42	
N4	HG/T 20592-2009	法兰 WN 50(B)-16 RF S=6	1	S30408II		2.5	
		接管 $\phi 57 \times 6$	1	S30408		1.16	
N3	HG/T 20592-2009	法兰 WN 50(B)-16 RF S=6	1	S30408II		2.5	
		接管 $\phi 57 \times 6$	1	S30408		2.42	
N2		筋板 40X6	2	S30408	0.6	1.2	
		接管 $\phi 57 \times 6$	1	S30408		3.55	
	GB/T 12459-2017	弯头CF304-DN50-III-6 90EL	1	S30408		0.9	
		接管 $\phi 57 \times 6$	1	S30408		2.94	
	HG/T 20592-2009	法兰 WN 50(B)-16 RF S=6	1	S30408II		2.5	
N1	JB/T 4736-2002	补强圈 dN80X14-D	1	S30408		2.1	
	HG/T 20592-2009	法兰 WN 89(B)-16 RF S=7	1	S30408II		4.0	
		接管 $\phi 89 \times 7$	1	S30408		2.8	
11		接地板 1=8	2	S30408	0.13	0.26	
10	本图	梯子 $\phi 16$	3	S30408	1.78	5.34	
9	本图	把手 $\phi 12$	3	S30408	0.62	1.86	
8	03.276-3	保温圈组件	1	Q235B		234	
7	HG/T 21574-2018	塑料板扶手 SP-5-15	2	Q235B/S30408	33.5	67	注2
6		黄板 DN4000 I=14 H=3920	1	S30408		5489	
5	JB/T 4736-2002	补强圈 dN600X14-D	1	S30408		48.2	
4	HG/T21520-2014	法兰 WN (WN-RS/S30408) 600-16	1	组合件		432	注3
3	GB/T 25198-2010	碳钢法兰 EHA4000X16(13.44)	2	S30408	2189	4378	
2	03.276-4	铭牌组件	1	组合件		3.48	
1	03.276-3	插座组件	1	组合件		3283	
件 号	图号或标准号	名 称	数量	材 料	单 量 (kg)	总 量	备 注
0	发布用于施工						2023.2.15
修改 REV. NO.	说明 DESCRIPTION	设计 DRAWN	校核 CHKD.	审核 APPR.	批准 AUTHORIZE	日期 ISSUE DATE	
中石化南京工程有限公司 SINOPEC NANJING ENGINEERING CO., LTD.							
催化剂公司天津新材料生产基地（一期）工程建设项目				未经SNEI书面许可,不得以任何方式复制或用于与本项目无关的其他用途。 DO NOT REPRODUCE OR EMPLOY FOR OTHER PURPOSES OTHER THAN THIS PROJECT WITHOUT WRITTEN CONSENT FROM SNEI			
甲类罐组 V-182108 乙二胺原料罐 V=67.02m³ 装配图（一）				设计阶段 DES. STAGE 详细设计 比例 SCALE 1:20 项目号 JOB. NO. 0321083 图号 DWG. NO. 0321083-182-0007-EQ-100-001 03.276-1			
业主文件号 OWNER'S DOC. NO.		TJ01-SNEI-DD-100182-EQDW-0007-01					