


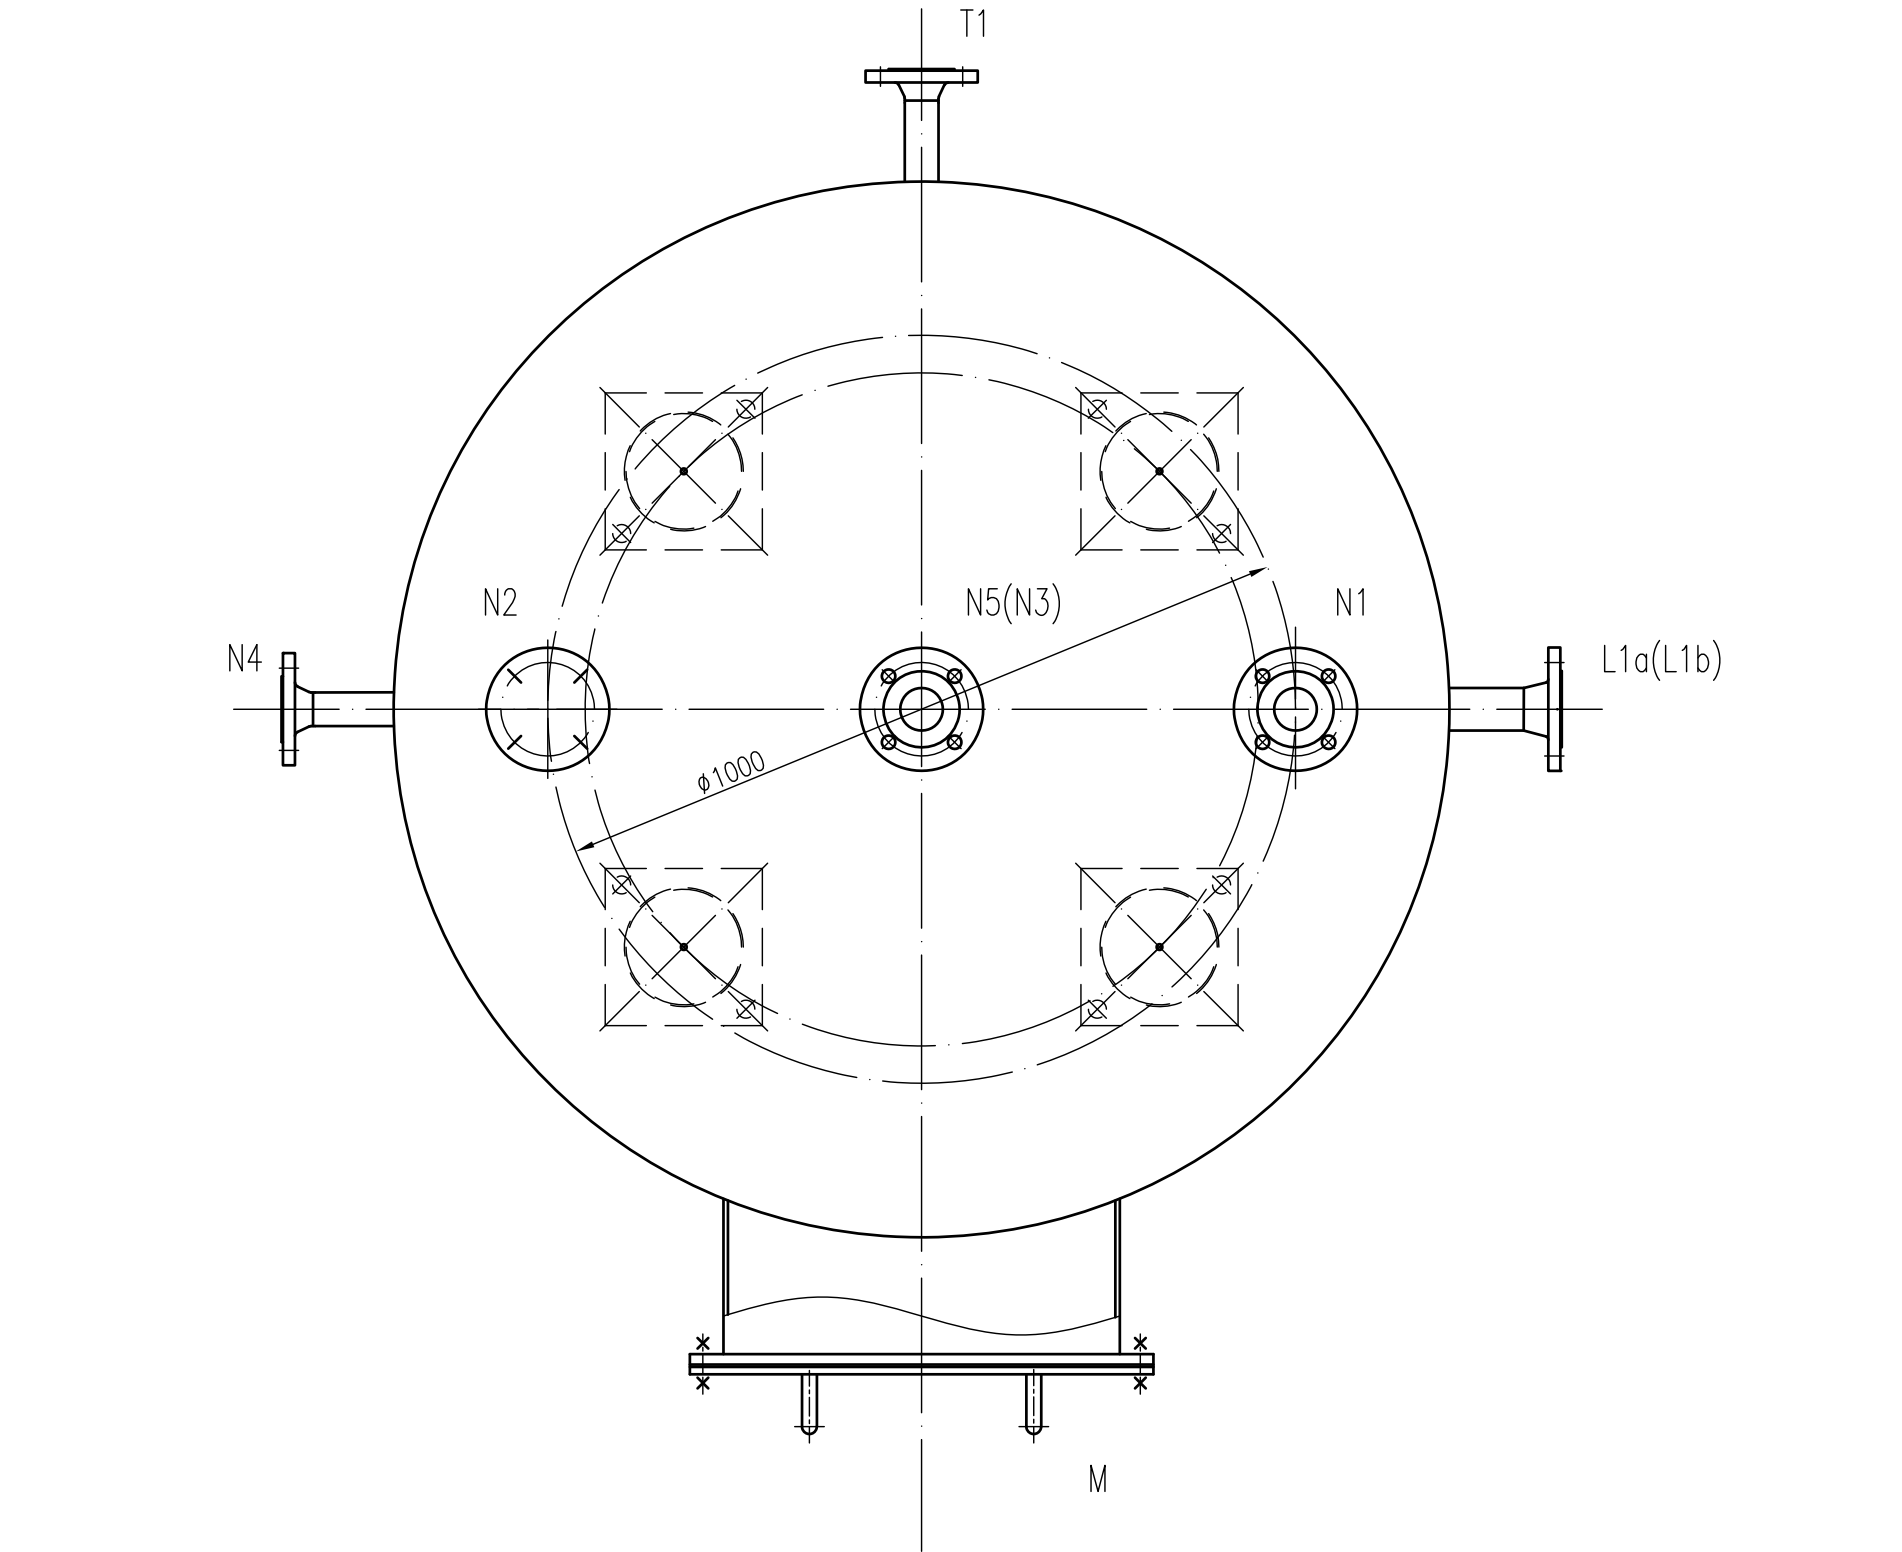


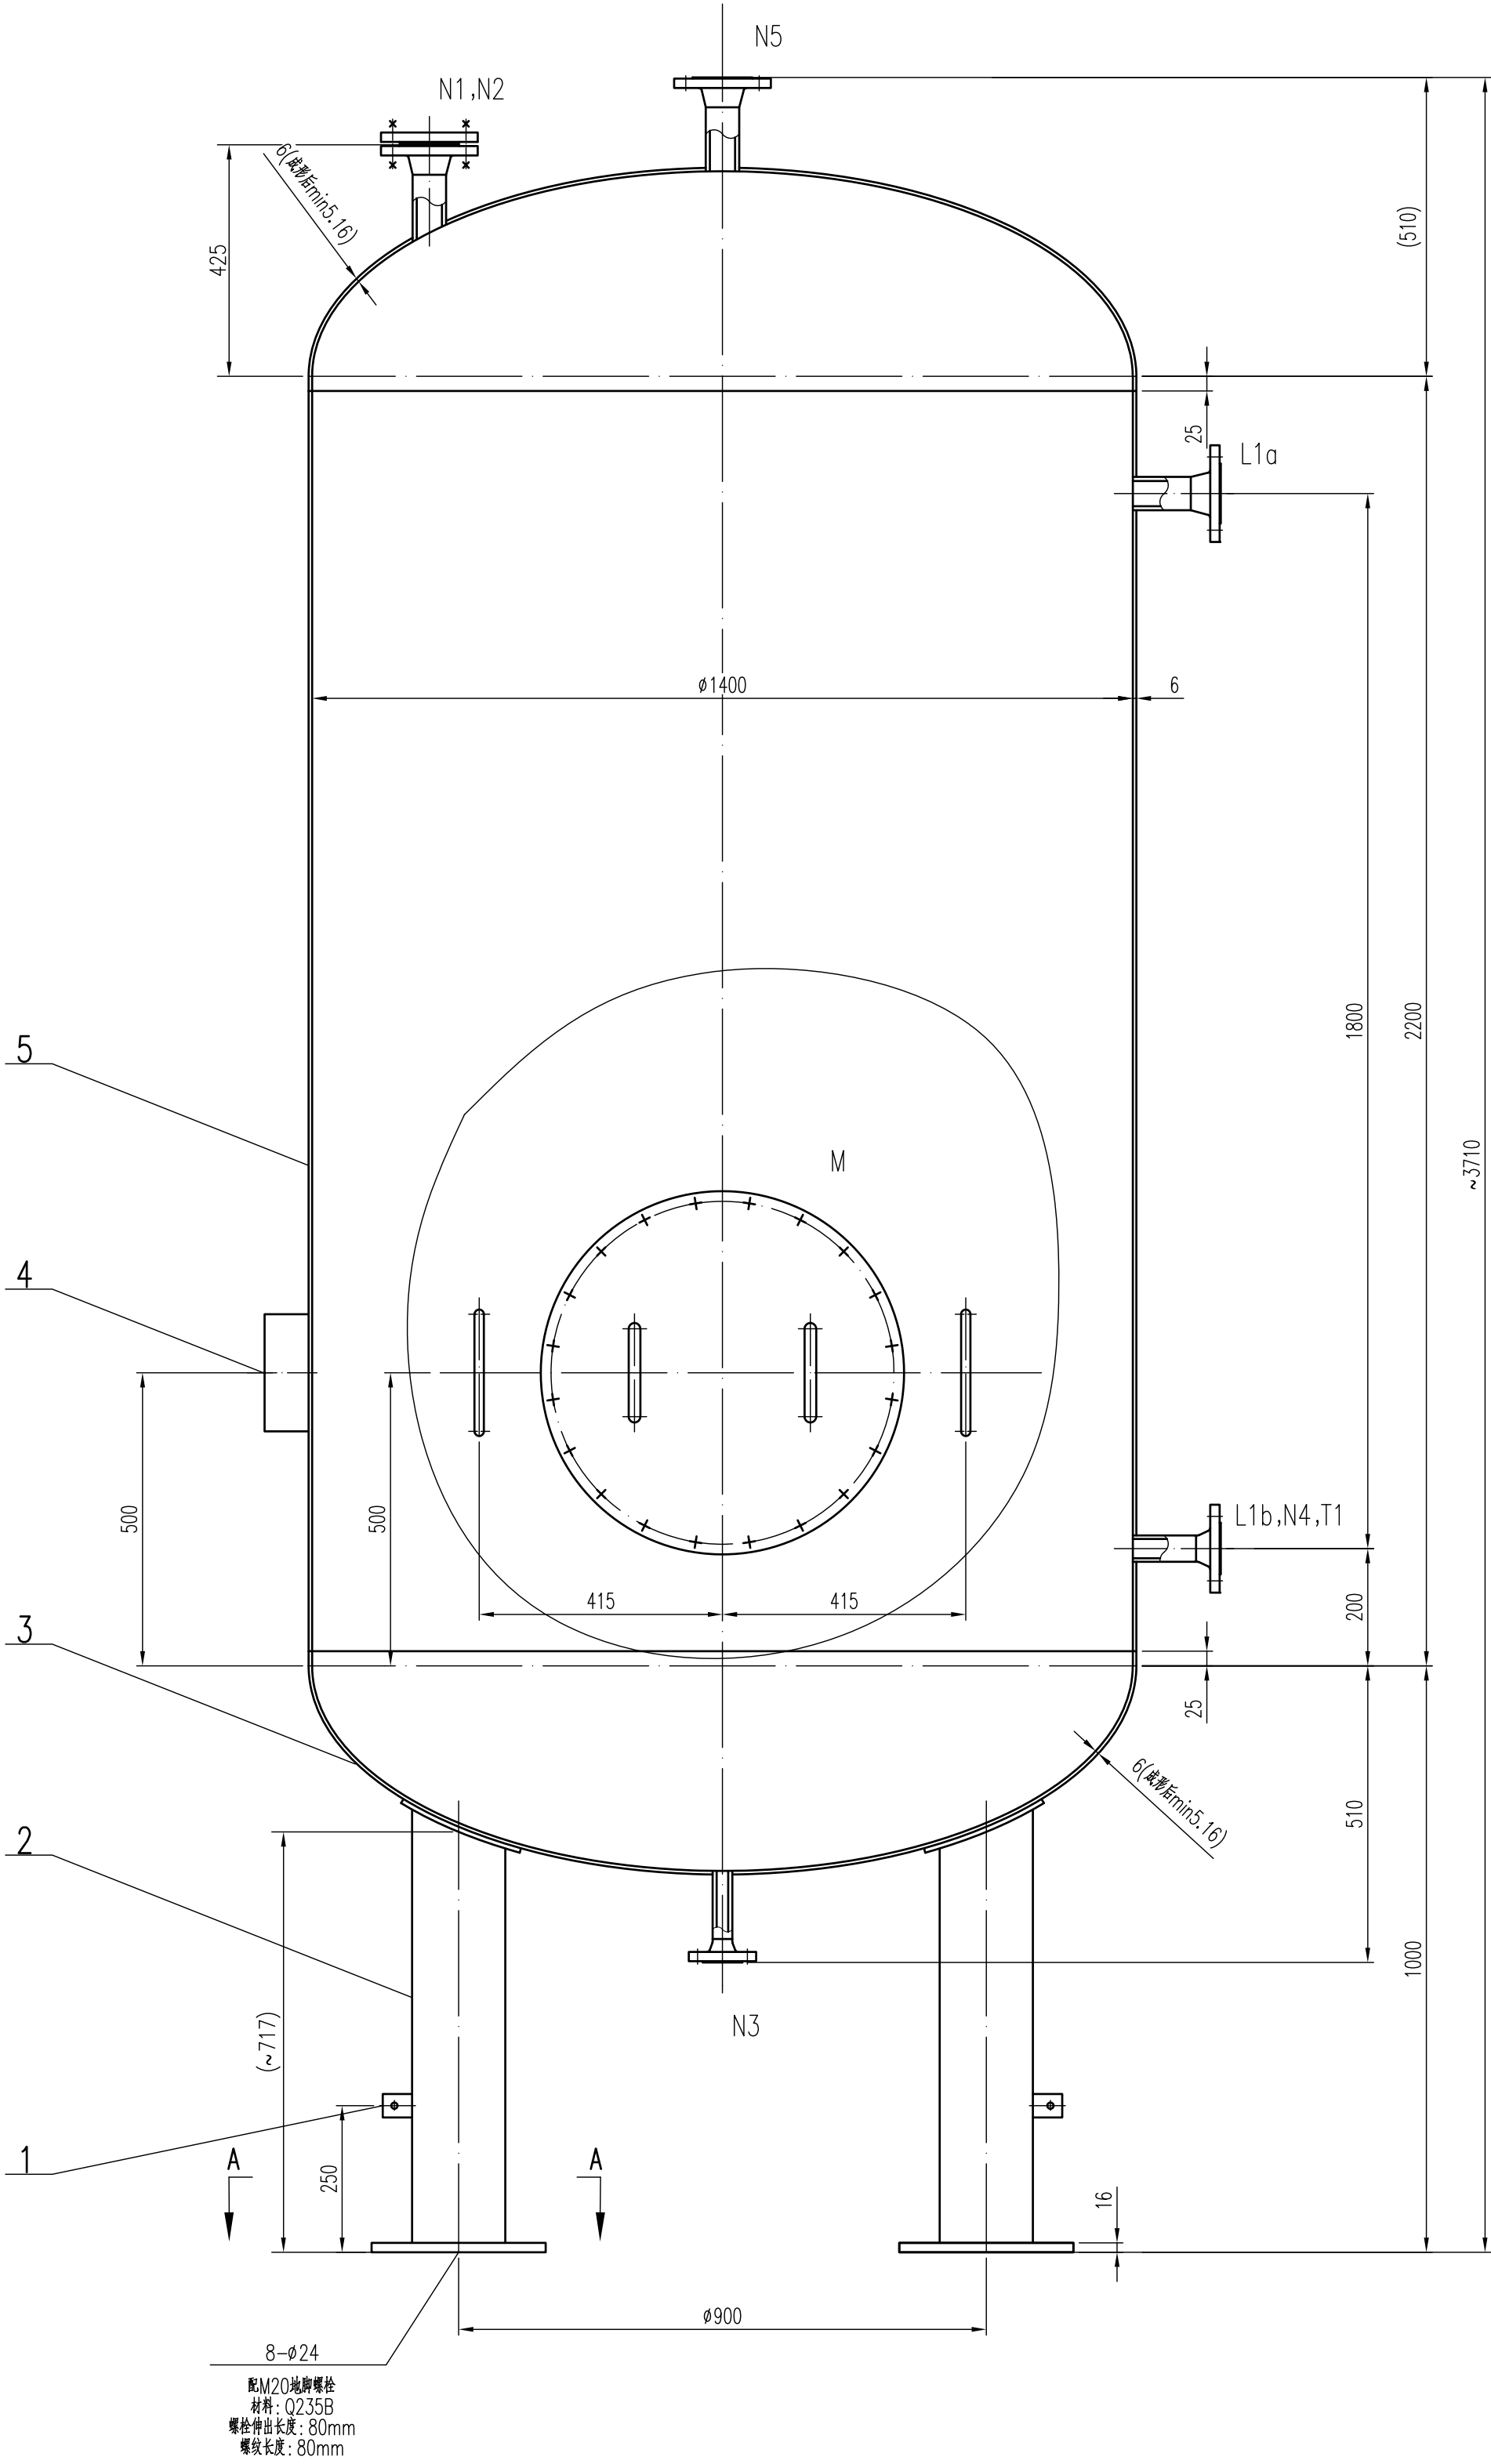


对接接头焊接详图

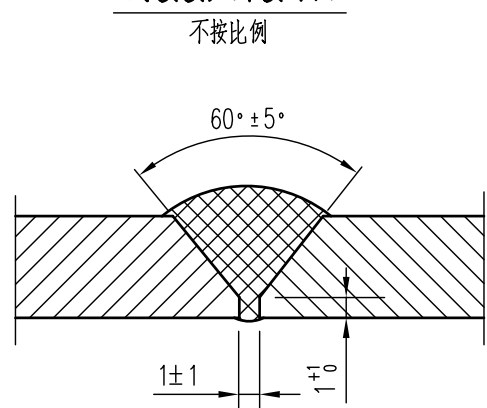


径向齐平接管焊接详图

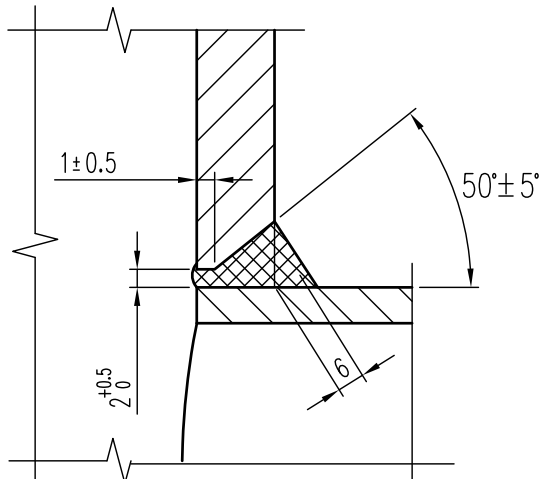


非径向齐平接管焊接详图

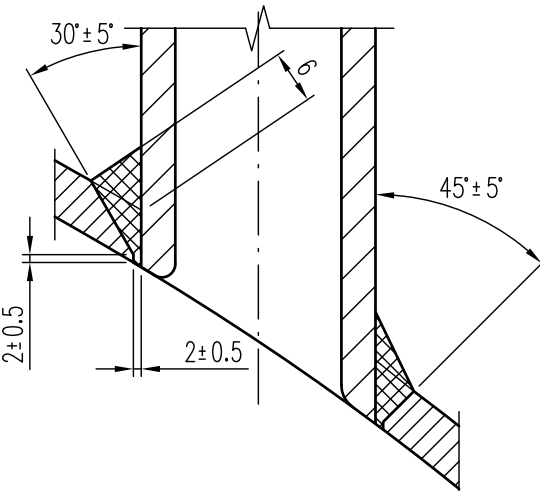

接地板详图

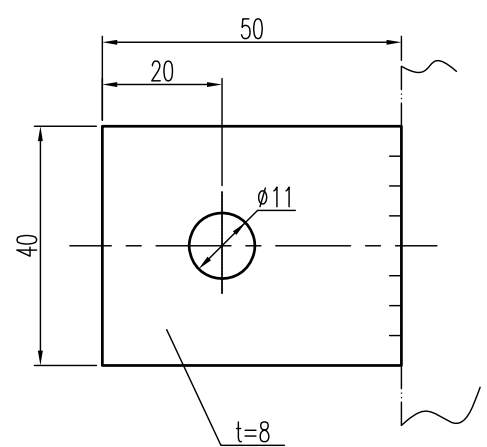

A-A

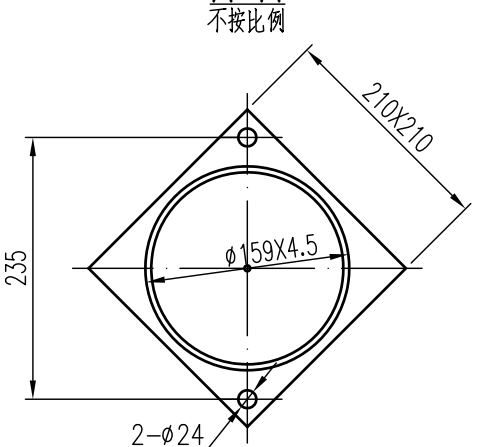

其它技术要求

- 所有承压焊接接头均需采用全焊透结构，不允许存在未焊透。
- 图中所述筒体名义厚度不包括冲压（制造）减薄量，钢板材料厚度由制造厂确定，封头的最小成形厚度不得小于图上所注厚度。
- 不锈钢材料及焊接接头应按GB/T4334-2020中方法E（铜-硫酸铜-16%硫酸铜试验方法）进行面间腐蚀倾向试验，考卷试验后，试样表面不得有晶间腐蚀现象。
- 设备水压试验时，应控制水中氯离子含量≤25mg/L。试验合格后，应立即将水渍去除干净。
- 设备制造完毕后，不锈钢部分应清除污垢，去油并进行酸洗钝化处理，所形成的钝化膜应采用蓝点法检查，无蓝点为合格。
- 其余尺寸公差按HG/T 20584-2020中第14章的要求。
- 法兰的螺栓孔应与壳体的主轴线或铅垂线均布。
- 本设备需设置防火层，防火层的耐火极限应≥2h，防火层按Q321083-000-0000-EQ-070-001《立式工艺设备防火涂料施工技术条件》进行施工和验收，且符合GB50160-2008《石油化工企业设计防火标准》（2018年版）的规定。
- 设备安装时，地脚螺栓应采用及螺母拧紧。
- 所有开孔不得位于对接焊缝。
- 在进入设备前应确认梯子、把手等辅助设施是否安全可靠。

管 口 表

符 号	公称压力 PN	公称尺寸 DN	法 兰 标 准	法兰类型 代号	密封面 型 式	用 途	接管外伸长度 (S.F. TO C.L.)	接管规格 (外径×壁厚)
M	—	500	—	—	—	人孔	—	φ530X6
N1	16	50	HG/T20592-2009	IF	RF	冷凝水入口	见图	φ70X8
N2	16	50	HG/T20592-2009	IF	RF	备用口(带法兰盖)	见图	φ70X8
N3	16	25	HG/T20592-2009	IF	RF	排液口	见图	φ36X7
N4	16	40	HG/T20592-2009	IF	RF	凝水出口	860	φ57X7.5
N5	16	50	HG/T20592-2009	IF	RF	排液口	见图	φ70X8
T1	16	40	HG/T20592-2009	IF	RF	就地温度计口	860	φ57X7.5
L1ab	16	50	HG/T20592-2009	IF	RF	就地液位计口	860	φ70X8

L1ab	HG/T 20592-2009	法兰 IF 50-16 RF	2	S30408II	2.5	5.0	
T1	HG/T 20592-2009	法兰 IF 40-16 RF	1	S30408II		2.0	
N5	HG/T 20592-2009	法兰 IF 50-16 RF	1	S30408II		2.5	
N4	HG/T 20592-2009	法兰 IF 40-16 RF	1	S30408II		2.0	
N3	HG/T 20592-2009	法兰 IF 25-16 RF	1	S30408II		1.0	
N2	GB/T 6170-2015	螺母 M16	4	8级	0.029	0.12	
	GB/T 5782-2016	六角螺栓 M16X60	4	8.8级	0.14	0.564	
	HG/T 20606-2009	垫片 RF 50-16	1	RSB/30408		—	
	HG/T 20592-2009	法兰盖 BL 50-16 RF	1	S30408		3.0	
N1	HG/T 20592-2009	法兰 IF 50-16 RF	1	S30408II		2.5	
	HG/T 20592-2009	法兰 IF 50-16 RF	1	S30408II		2.5	
M	HG/T 21515-2014	人孔 vmb1NM-RSB/S30408I 500	1	组合作		52	
5		筒体 DN=1400 t=6 H=2150	1	S30408		452	
4	25.918-2	铭牌组件	1	组合作		2.5	
3	GB/T 25198-2010	翻圈转头 EHA1400X6(5.16)	2	S30408		102.9	2.06
2	NB/T47065.4-2018	支座 B3 h=717	4	10.0235B/S30408		20.0	80.0
1		接地板 t=8	2	S30408		0.13	0.26
件 号	图号或标准号	名 称	数 量	材 料	单 重 (kg)	总 重	备 注

0	发布用于施工	宋琪	刘姚军	郭红玲			2023.02.10
修改 REV. NO.	说明 DESCRIPTION	设计 DRAWN	校核 CHKD.	审核 APPR.	批准 AUTHORIZE		日期 ISSUE DATE

中石化南京工程有限公司 SINOPEC NANJING ENGINEERING CO., LTD.											
催化剂公司天津新材料生产基地（一期）工程建设项目											
200吨/年BCE催化剂 V-440511 常压不锈钢冷凝水罐 V=4.10m³ 装配图				设计阶段 DES. STAGE		详细设计		专业 DISP.		设备	
				比例 SCALE		1:10		第 1 张 SHEET		共 1 张 OF 1	
				项目号 JOB. NO.		0321083		◇			
				图号 DNG. NO.		25.918-1					
业主文件号 OWNER'S DOC. NO.				TJ01-SNEI-DD-400440-EQDW-0112-01							